



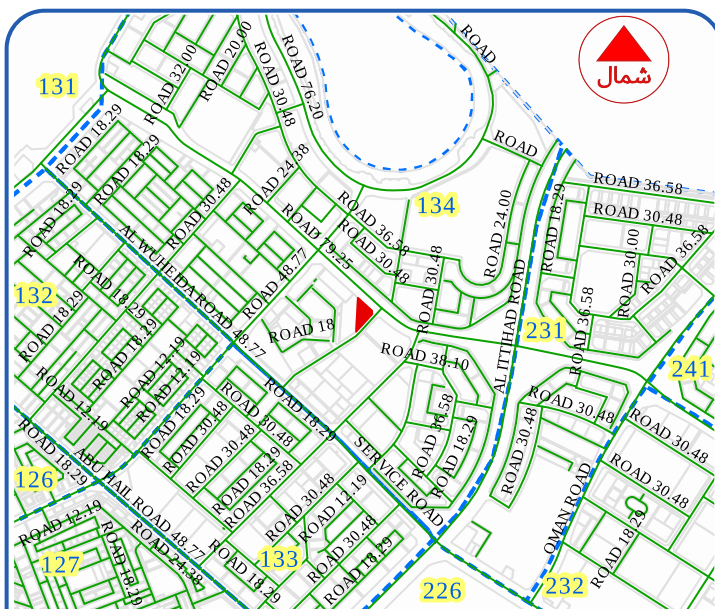

الموقع العام
GENERAL AREA

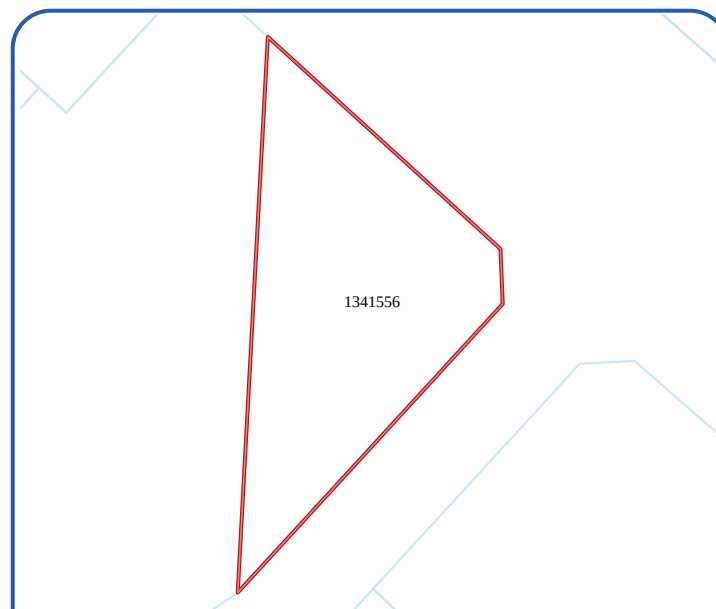


المسح الطبوغرافي
TOPOGRAPHIC MAP

الاستعمال Landuse	RC2/18	تجاري , مكاتب , سكني
الارتفاع Height	RC2/18	أرضي + أول لقاعدة البرج + (16) طابق وبنسبة طابقية = 5.0
المواقف Parking	RC2/18	موقف لكل شقة و لكل استوديو و موقفين لكل شقة تزيد مساحتها عن 150 متر مربع و موقف لكل 70 متر مربع من الاستعمال التجاري و موقف لكل 50 متر مربع للإستعمال المكتبي
الارتداد Setback	RC2/18	ربع الارتفاع من الجوار ومن منتصف السكك وبعده أقصى 7.5 متر و بحد أدنى 3 متر
الملاحظات Remarks	RC2/18	يجب الحصول على موافقة جهاز الخدمات التالية : هيئة الطرق و المواصلات , هيئة كهرباء و مياه دبي , هيئة الطيران المدني , بلدية دبي / إدارة الصرف الصحي قبل الترخيص

الأرض تقع ضمن المنطقة الساحلية وفقاً للمرسوم رقم 22/2001. و يتوجب الحصول على شهادة عدم ممانعة من إدارة الشواطئ العامة و القنوات المائية بلدية دبي قبل المباشرة بالعمل المنسوب المرجعي = (30) سم من منسوب أي طريق قائم مجاور يتحمل المالك تكاليف نقل خطوط الخدمات إن وجدت.

هذه المعلومات التخطيطية سارية المفعول ما لم تتعارض مع التشريعات التخطيطية المعتمدة، و للتأكد من صلاحيتها قبل البيع والشراء يرجى استخدام تطبيق بلدية دبي الموحد (خريطتي).

The information is applicable as long as it does not conflict with other approved planning regulations, and should always be reviewed for validity. Upon selling or purchasing please use Dubai Municipality Unified Application (Kharetati).

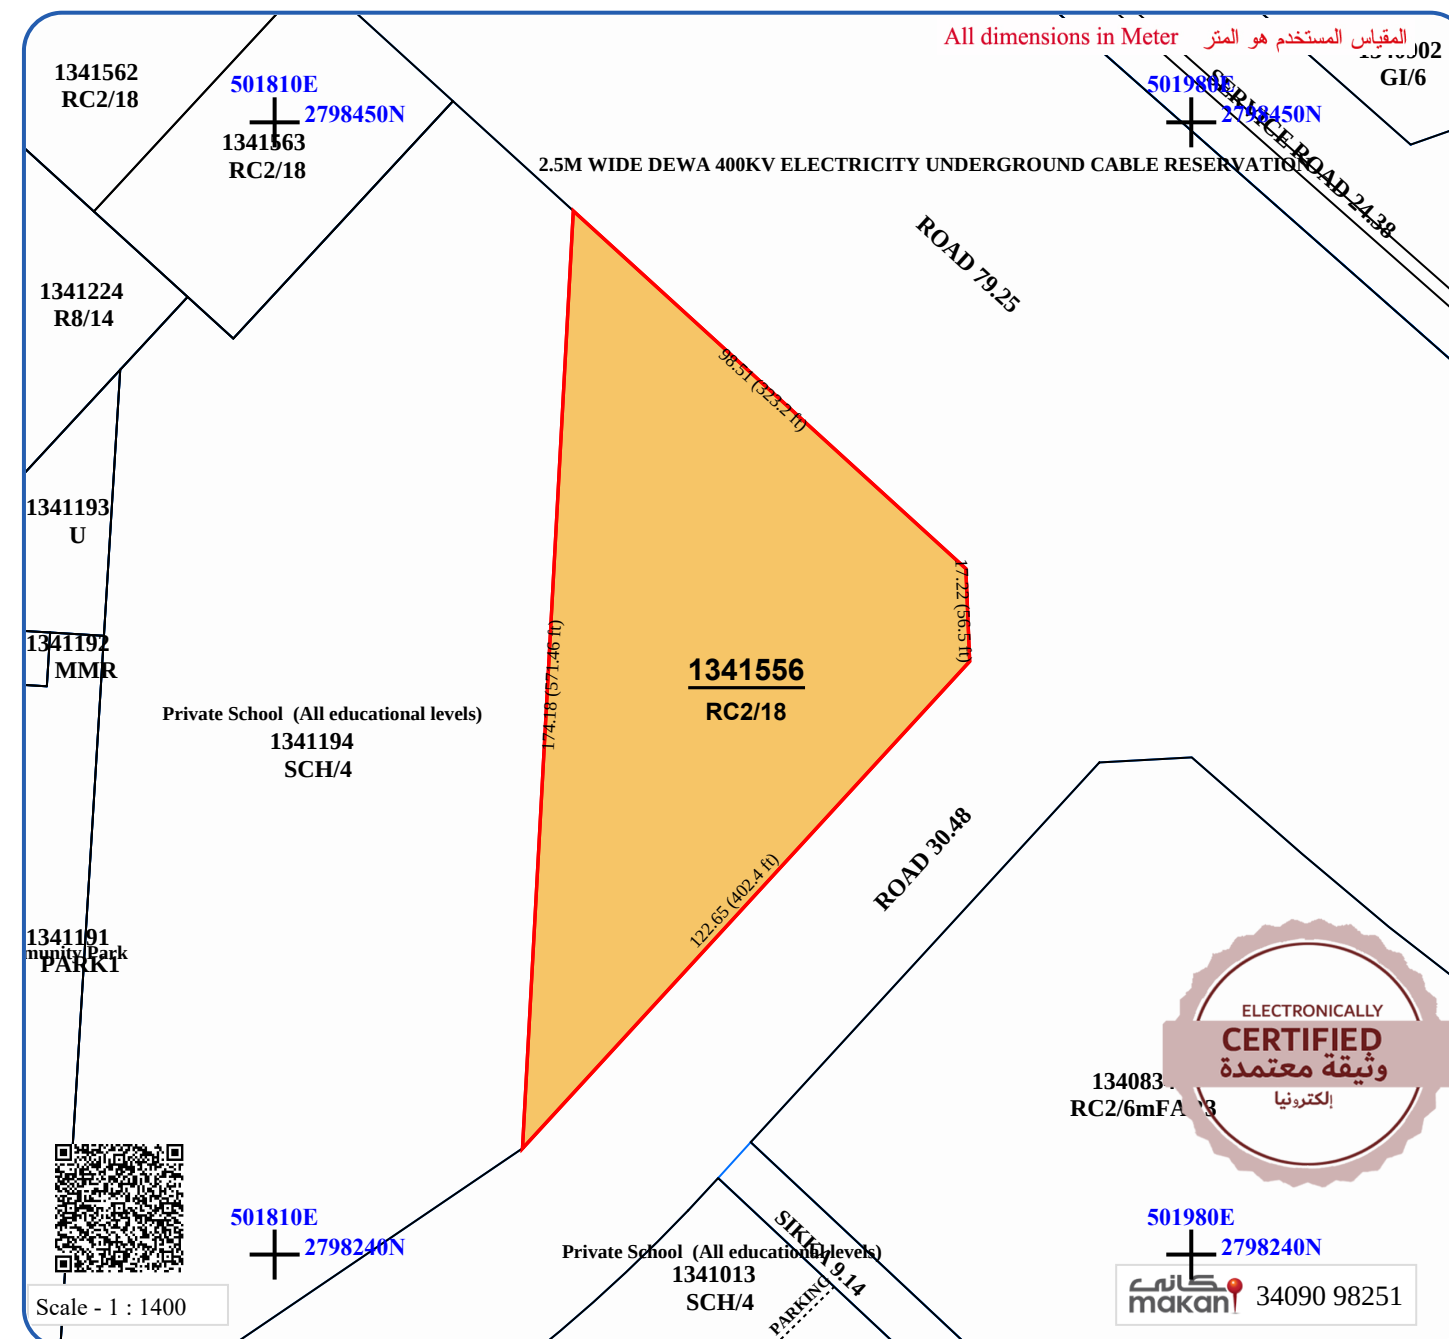

PLEASE SCAN THE QR CODE TO VIEW THE INFRASTRUCTURE MAP,
SITE PLAN DIGITAL COPY, DIMENSIONS FILE AND OTHER
INFORMATION.

يرجى مسح (رمز الاستجابة السريع) لعرض خارطة البنية التحتية والمعلومات الأخرى.

تاریخ الاصدار Issue Date	ملاحظات Remarks
-----------------------------	--------------------

المالك : مؤسسة دبي الرياضية
Owner : DUBAI SPORTS CORPORATION

المساحة الكلية Total Area	المساحة المتأثرة Affected Area	مساحة إرتداد السكة Sikka Setback	مساحة التعويض أكثر Compensation Area	المساحة المتبقية للبناء Balance Area Can Be Built
7389.43 SQ.M	NIL	NIL	NIL	7389.43 SQ.M
79539 SQ.F	NIL	NIL	NIL	79539 SQ.F