


PLOT NUMBER	6457790	
PLOT AREA	2,624.73 M ² (28,252.38 FT ²)	
MAX. GFA	13,935.45 M ² (149,999.94 FT ²)	
MAX. HEIGHT	G+3P+9	
MAX. COVERAGE	N/A	
SETBACK (M)	BUILDING	PODIUM
SIDE (1)	5	4
SIDE (2)	7	6
SIDE (3)	7	6
SIDE (4)	7	6
LAND USE / GFA SPLIT		
COMMERCIAL : RETAIL (1,680.00 M ²) RESIDENTIAL : APARTMENT (12,255.45 M ²)		
PLOT COORDINATES		
ID	EAST	NORTH
1	498814.961	2776592.090
2	498768.120	2776572.429
3	498748.123	2776620.070
4	498794.965	2776639.731

COORDINATES SYSTEM IS DLTM

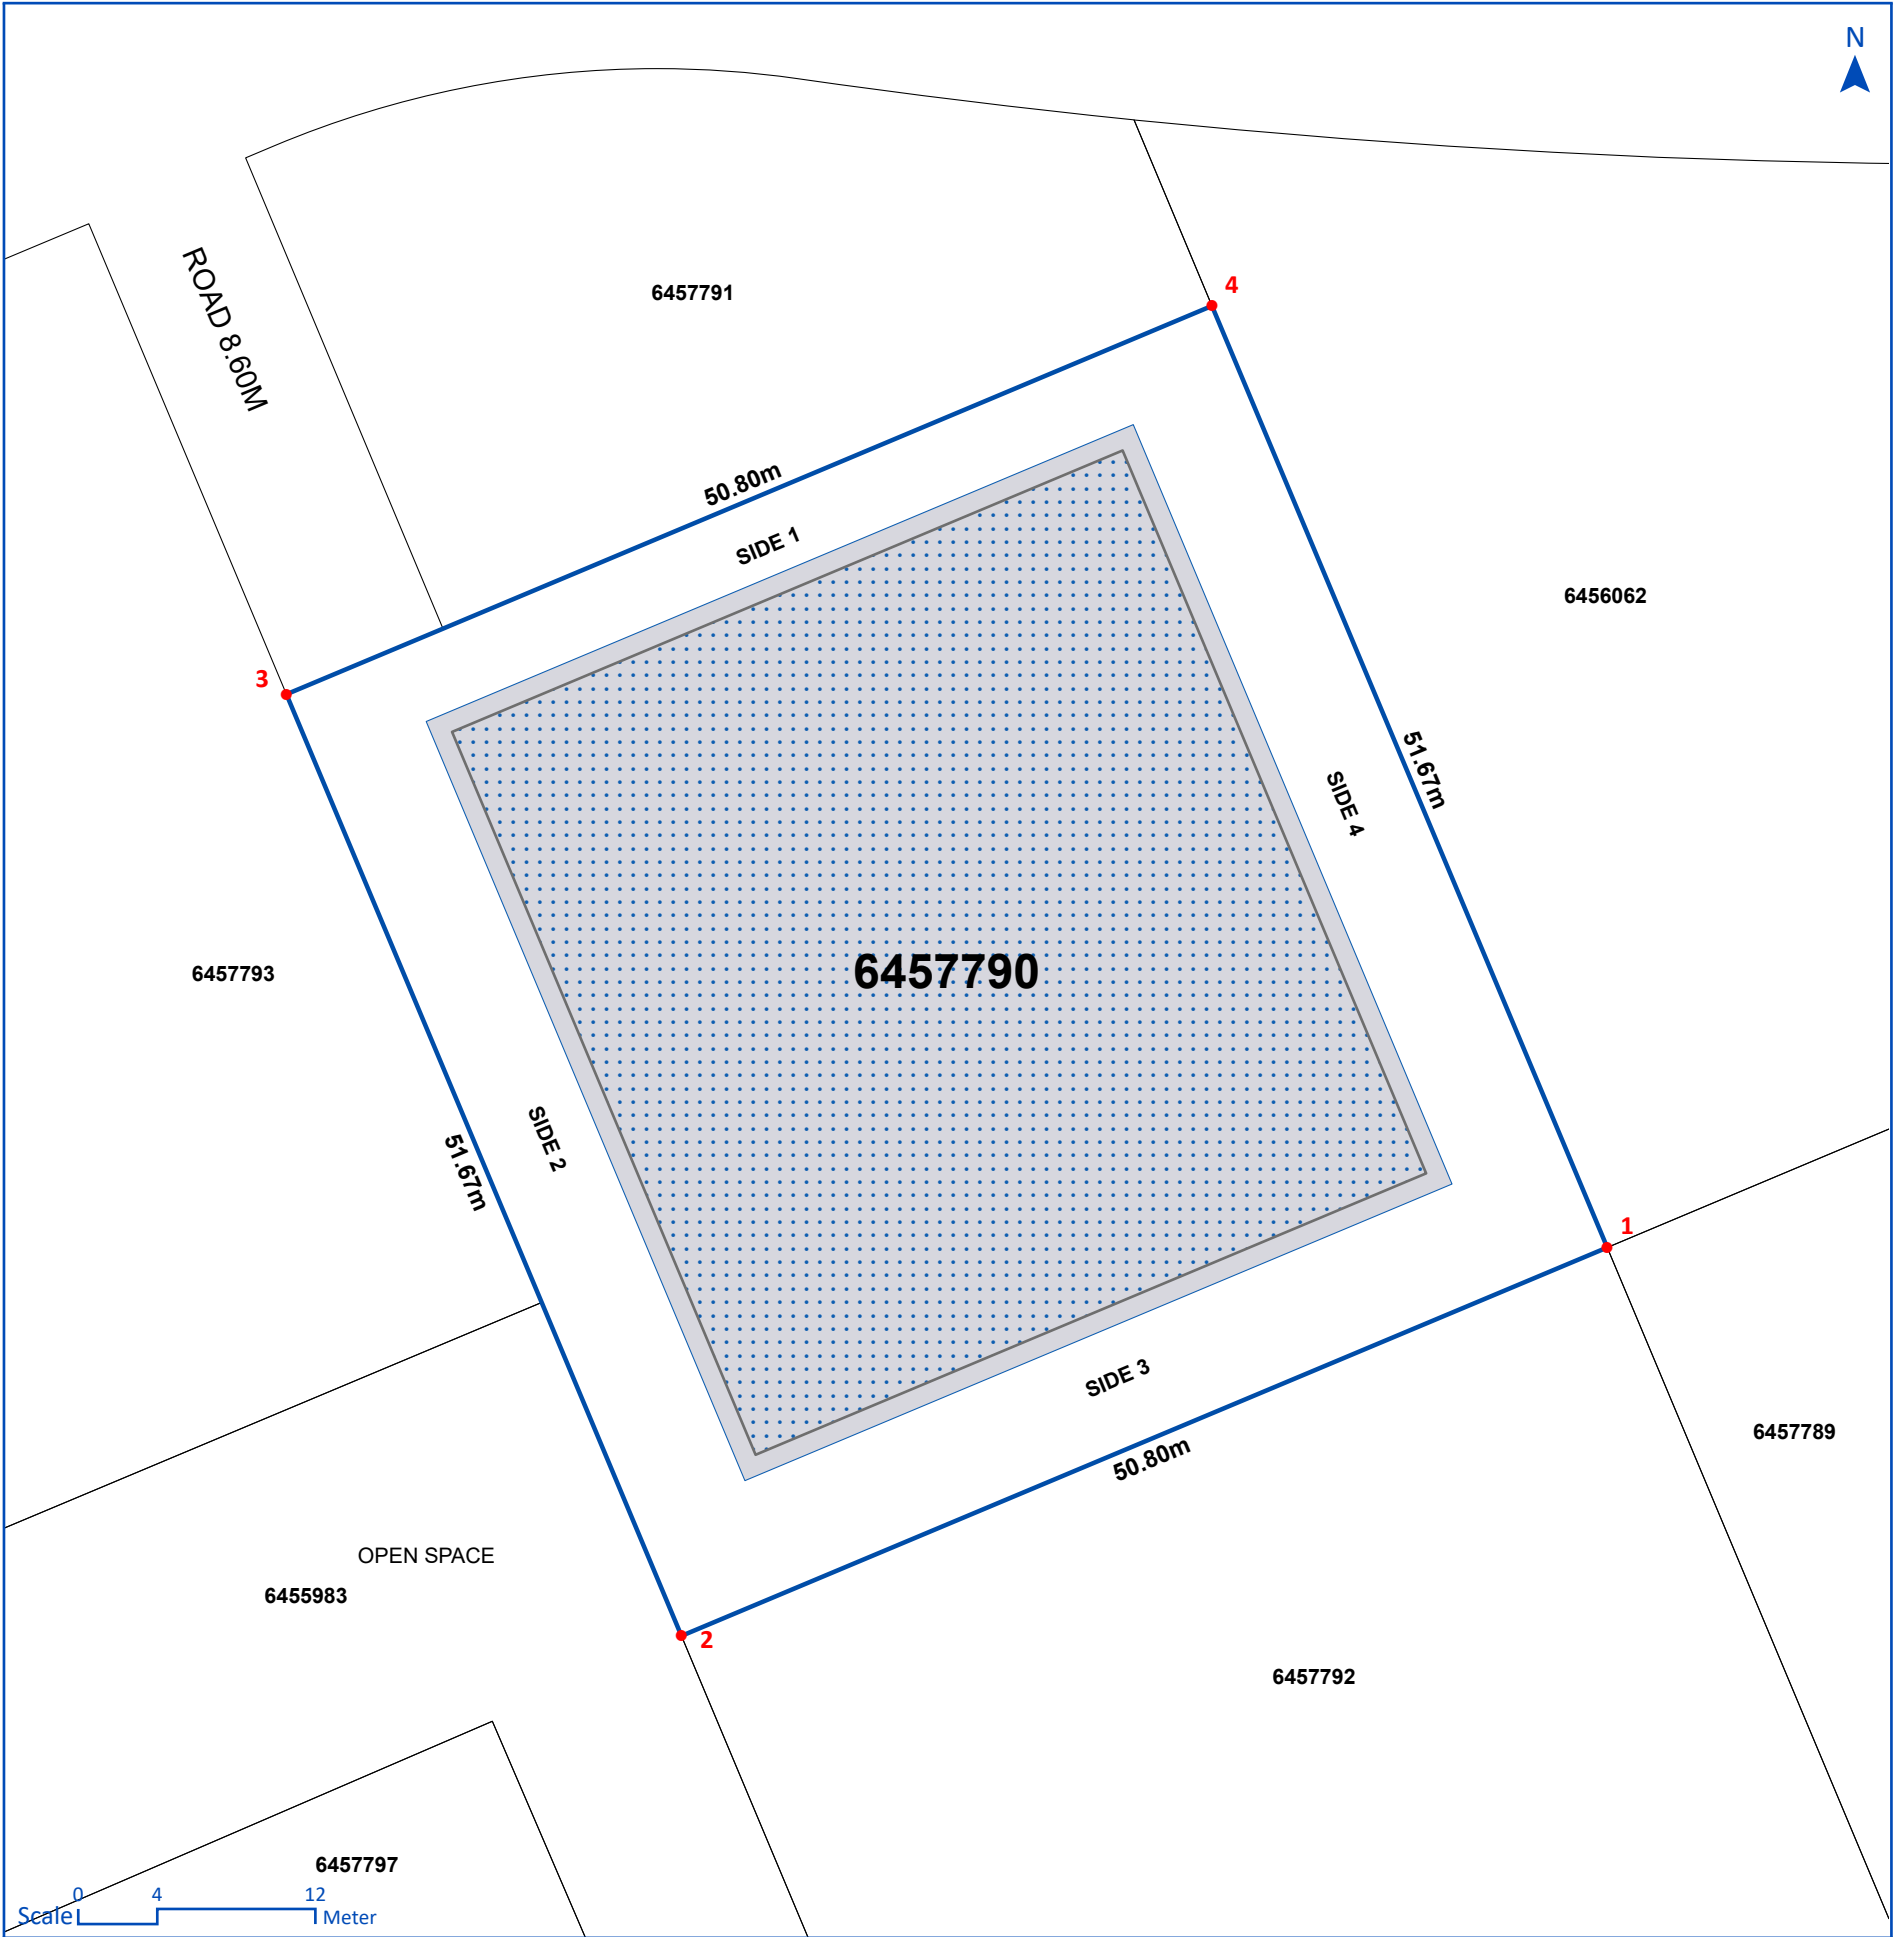

GENERAL NOTES	- PARKING: FOR APARTMENT, ONE BAY FOR EACH UNIT LESS THAN OR EQUAL TO 150 SQ.M GFA AND TWO BAYS FOR EACH UNIT EXCEEDING 150 SQ.M GFA; FOR RETAIL, ONE BAY FOR EACH 70 SQ.M OF RETAIL NET AREA. - THIS SITE PLAN TO BE READ IN CONJUNCTION WITH THE PLOT GUIDELINES FOR ADDITIONAL INFORMATION. - RETAIL IS RESTRICTED ON THE GROUND FLOOR ONLY.
	THIS DOCUMENT IS FOR ILLUSTRATION PURPOSE. FINAL DATA CAN BE OBTAINED THROUGH SITE PLAN AND DEMARCATION CERTIFICATES REQUESTS.



سلطة دبي للتطوير
Dubai Development Authority

GOVERNMENT OF DUBAI

Plot Details


MASTER DEVELOPER

LIWAN (L.L.C)

PROJECT NAME

MAJAN

LOCATION MAP

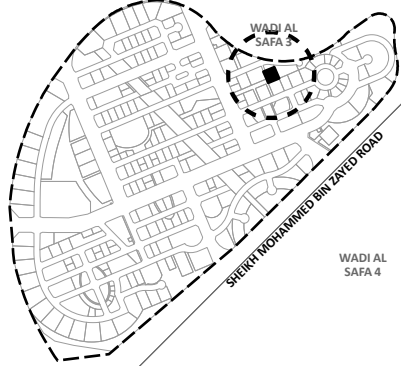

COMMUNITY

WADI AL SAFA 3

LEGEND

 PROJECT LIMIT

 PLOT

 PODIUM LIMIT

 BUILDING LIMIT



For live information please scan the QR code or visit
<https://gis.dda.gov.ae/dis/?PlotNumber=6457790>

ISSUE DATE

12/12/2023 09:45:41 PM